CORTE LONGITUDINAL

SECCION Y-Y´

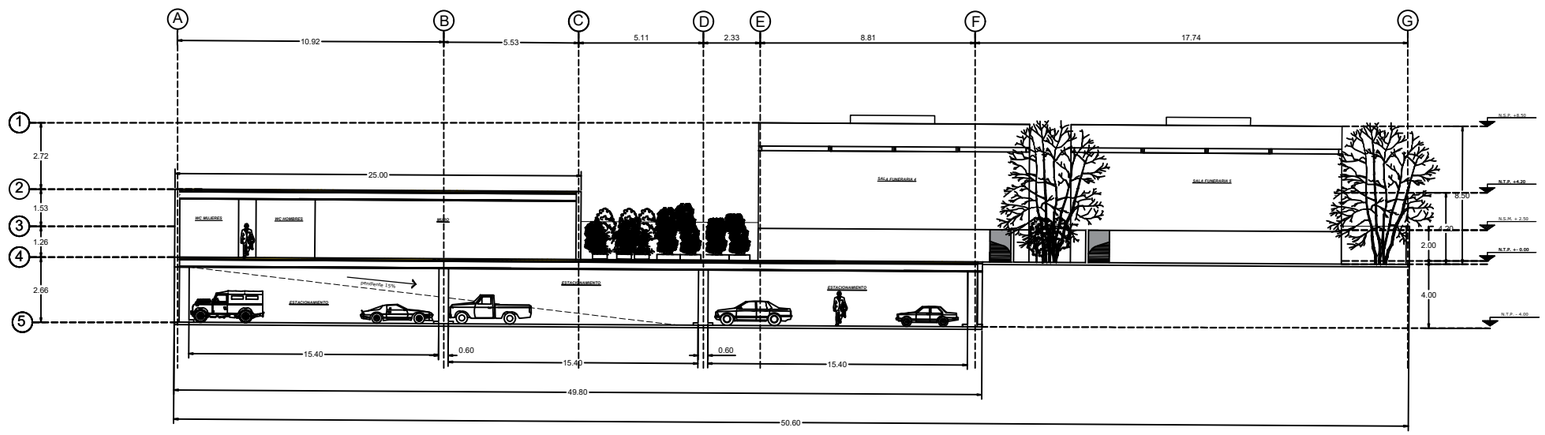

ANAYA +
PARTNERS
ARCHITECTURE

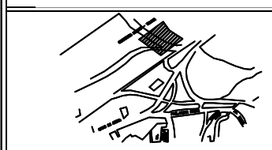

Dirección:
Carretera México-Toluca 5210, La Rosita
05320, Cuajimalpa de Morelos, CDMX, México.

Simbologia:

N.S.P. NIVEL SUPERIOR DE PRETIL

N.L.B.L. NIVEL LECHO BAJO DE LOSA

N.T.P. NIVEL TERMINADO DE PISO

CAMBIO DE NIVEL

F FIJA

Notas:

Proyectó:
Alejandro Anaya Arroyo
Diseñó:
Alejandro Anaya Arroyo
Revisó
Arq. Ivan Islas Garduño

Propietario:
Jorge Pablo Peña

Proyecto:
Funeraria
Tipo de obra:
Obra Comercial
Uso:
HM/5/40

Superficie del terreno:
6286m^2
C.O.S:

C.U.S:

D.R.O.:	C.S.E.:
C.I.:	C.D.U.y.A.:

Plano:
Arquitectónico

Escala:	Acotación:	Fecha:
1:150	Metros	Marzo 2026

Escala Gráfica:
0 0.30 1.0 1.50 3

Clave:
CO - 02